


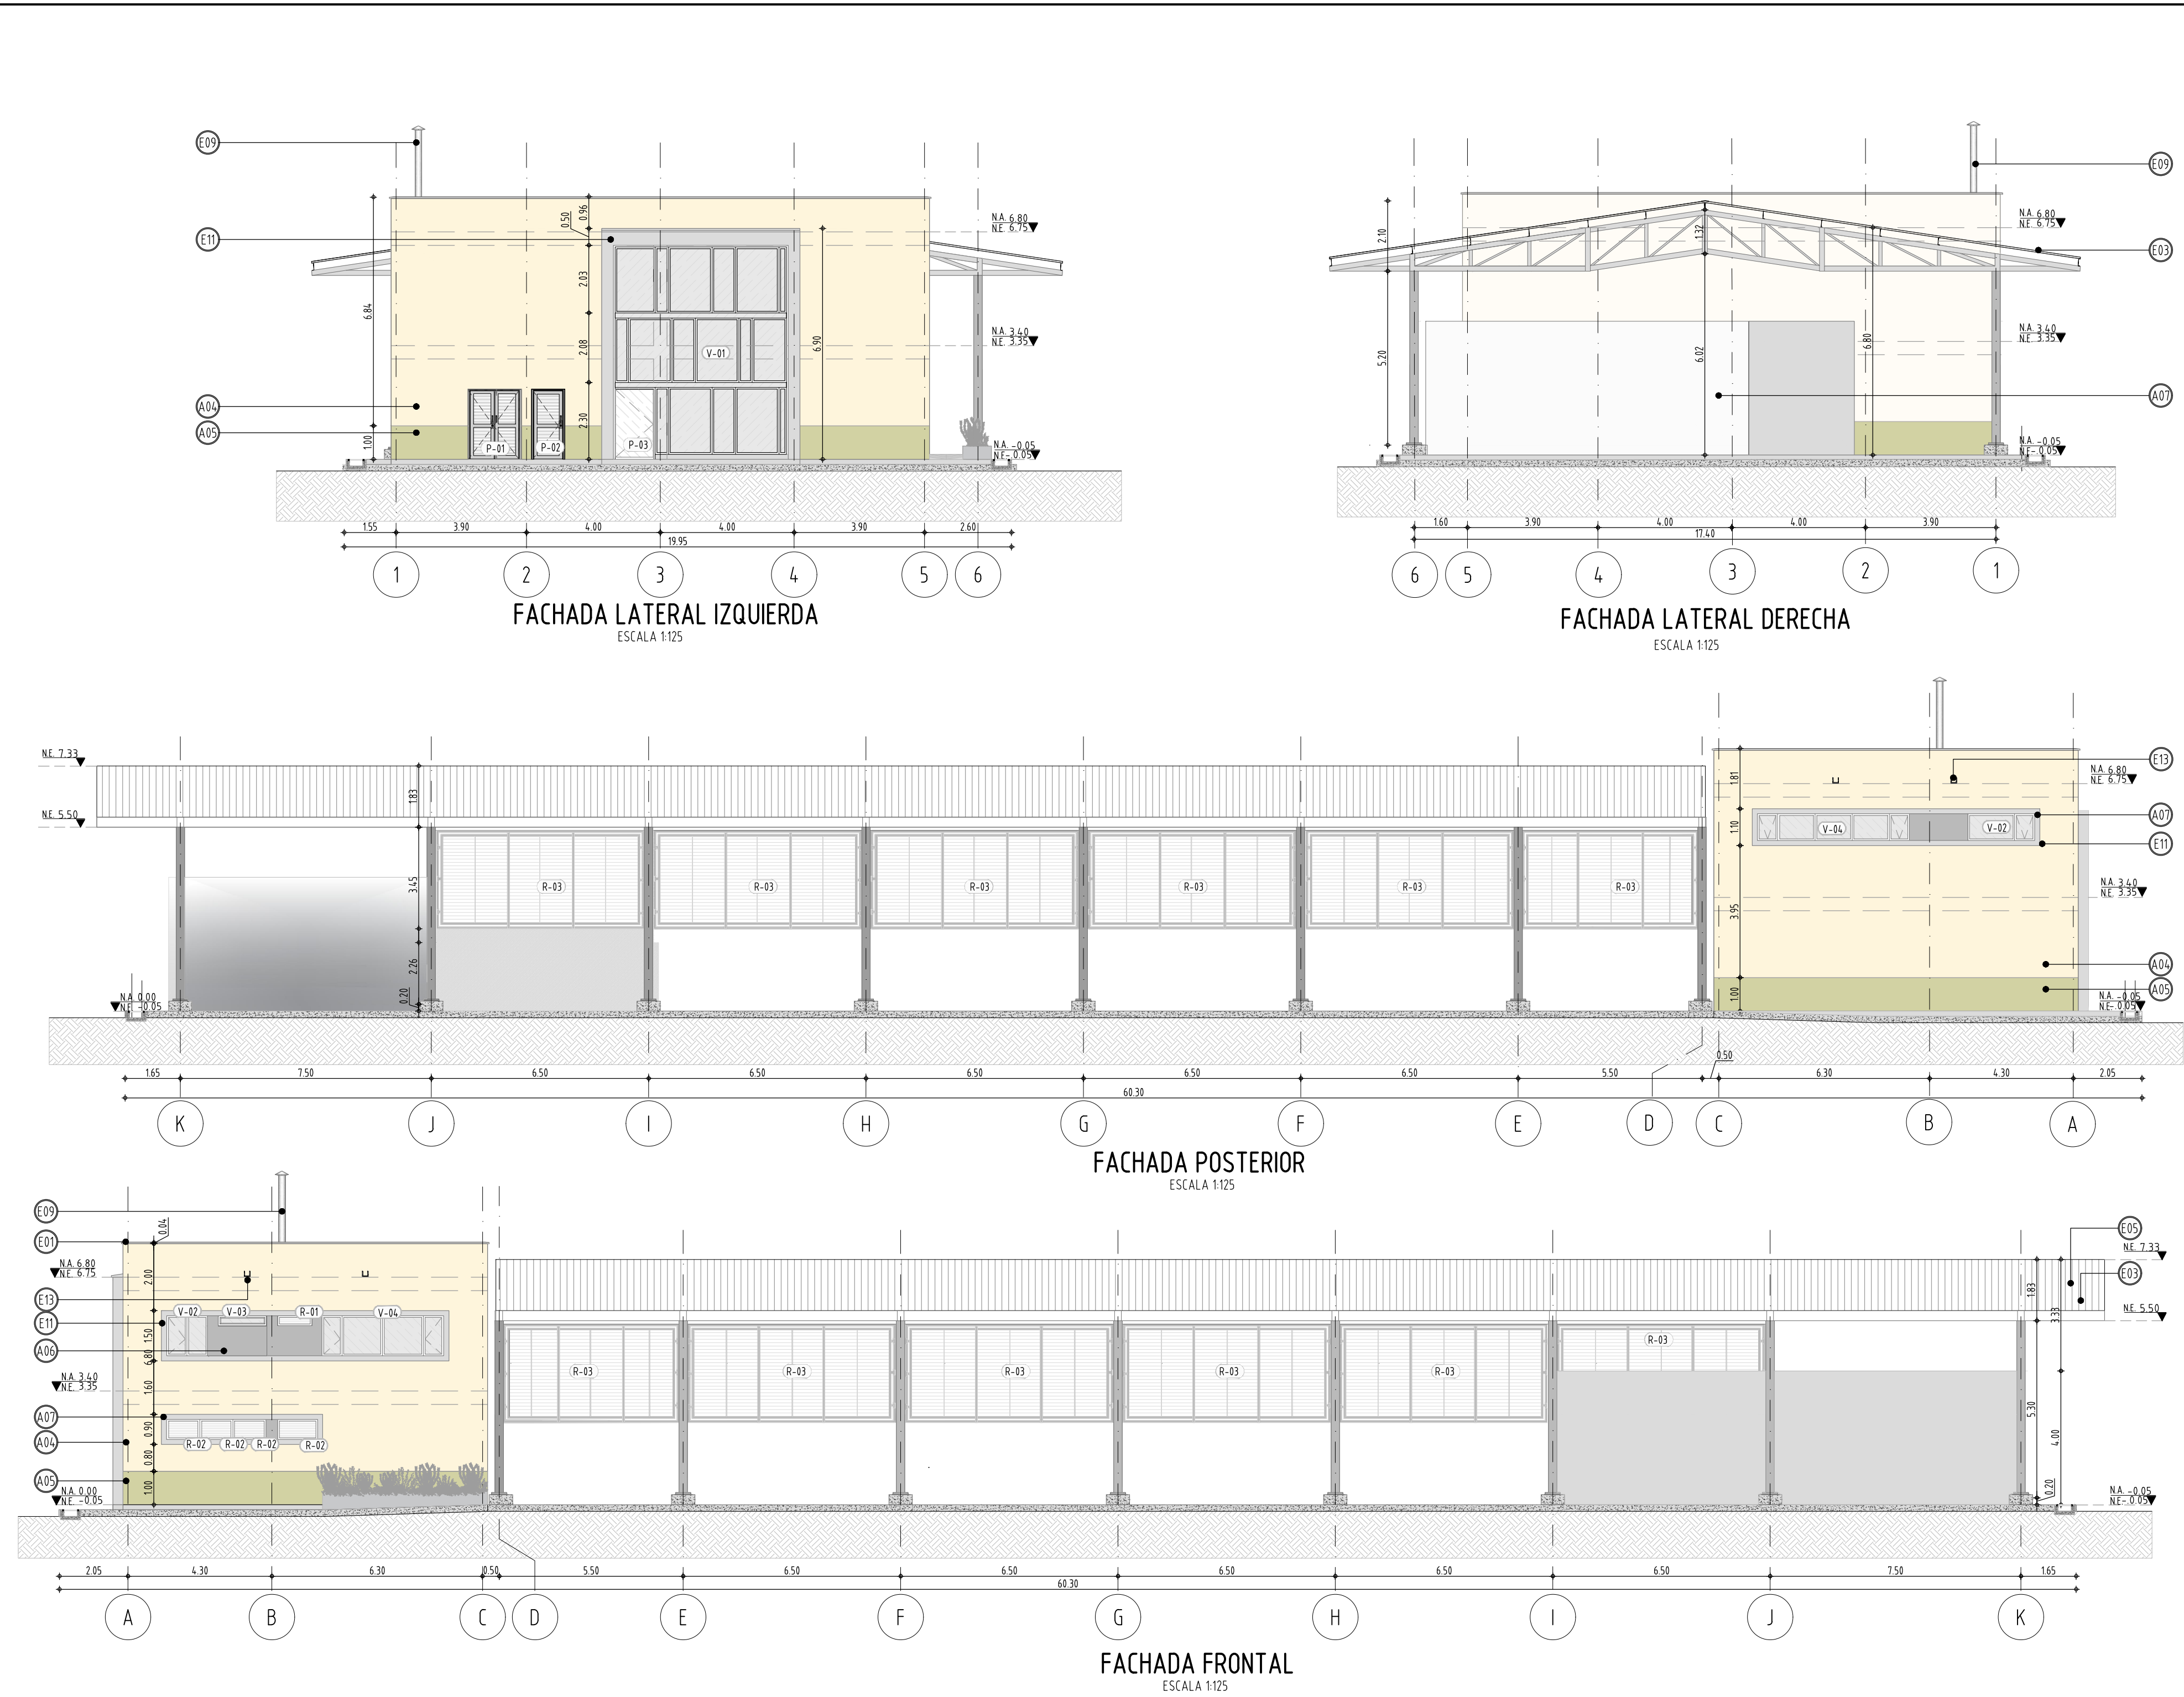

ACABADOS DE MUROS	
(M01)	MURO EN BLOQUE No. 5 Arcilla 33x23x11.5 cm. Incluye mortero de pega y grafil 5 mm.
(M02)	MURO EN BLOQUE CONCRETO ESTRUCTURAL LISO 12x19x39 cm. (Incluye mortero de pega y grafil)
(A01)	PANETE LISO 1:3 INT. + ESTUCO Y VINILO 3 MANOS SOBRE MURO INT. (Incluye estuco, 1 mano en pintura tipo 2 y dos manos en pintura tipo 1, filos y dilataciones) - color blanco almendra.
(A02)	PANETE LISO 1:3 IMPERMEABILIZADO + CERÁMICA HD BLANCO SATINADO Incluye boquilla blanca y pegante - Altura de instal. hasta H= 2,10 m, según diseño. + estuco plástico y pintura epóxica a 3 manos sobre muro int. desde H=2,10 m hasta nivel de borde inferior de vigas de placa superior - color blanco almendra.
(A03)	ESTUCO PLÁSTICO Y PINTURA EPÓXICA A 3 MANOS SOBRE MURO INT. (Incluye estuco plástico, una mano en pintura tipo 2 y dos manos en pintura epoxi poliámda, base de agua, con catalizador, filos y dilataciones - color blanco almendra. sobre panete liso 1:3 impermeabilizado.
(A04)	PINTURA ACRILICA PARA EXTERIORES (5 años) 3 MANOS FACHADAS Incluye 1 mano en pintura tipo 2 y dos manos en pintura Acrilica para exteriores (5 años), filos y dilataciones. Color marfil - RAL 1014 sobre panete impermeabilizado
(A05)	PINTURA ACRILICA PARA EXTERIORES (5 años) 3 MANOS FACHADAS Incluye 1 mano en pintura tipo 2 y dos manos en pintura Acrilica para exteriores (5 años), filos y dilataciones. Color verde ciprés, RAL 6011 sobre panete imperm.
(A06)	PINTURA ACRILICA PARA EXTERIORES (5 años) 3 MANOS FACHADAS Incluye 1 mano en pintura tipo 2 y dos manos en pintura Acrilica para exteriores (5 años), filos y dilataciones. Color gris oscuro RAL 7012 sobre panete imperm.
(A07)	PINTURA ACRILICA PARA EXTERIORES (5 años) 3 MANOS FACHADAS Incluye 1 mano en pintura tipo 2 y dos manos en pintura Acrilica para exteriores (5 años), filos y dilataciones. Color gris RAL 9006 sobre panete impermeabilizado.

ACABADOS DE CIELORASOS	
(C01)	PINTURA EPOXICA ALTA RESISTENCIA CON CATALIZADOR 3 MANOS Bajo Placa (Incluye 1 mano en pintura tipo 2 y dos manos en pintura epoxi poliámda con catalizador, filos y dilataciones, incluye resane y maquillaje de torta inferior
(C02)	SIN CIELORASO

ACABADOS DE PISOS Y GUARDAESCOBAS	
(P01)	ENDURECEDOR COLOR (TONOS SEGUN DISEÑO EN PLANO DE PISOS) Losa en concreto tipo Rocktop de Toxement o equivalente, acabado con allanadora metálica + pintura de señalización (según plano de pisos)
(P02)	PISO EN GRANO DE MARMOL GRAN TERRAZO GRIS CEARA color gris claro 40 x 60 cm. SKU 225026342 Ref. Alfa, equivalente o superior (Incluye destroncada, pulida y brillada, mortero de nivelación y dilatación en bronce).
(P03)	CERÁMICA MYSTIC GRIS LISA 30,5 X 60 CM. Incluye boquilla gris claro y pegante + alisado de piso en mortero 1:4 impermeabilizado E= 0.04 m - disposición según diseño.
(G01)	GUARDAESCOBA RECTO EN BALDOSA GRANO DE MARMOL PCL 5 Color negro san gil 40 x 10 cm. (Incluye boquilla y mortero de pega)
(G02)	GUARDAESCOBA EN PINTURA ESMALTE NEGRO MATE - H= 10 cm. Dilatación en panete (2cms prof. x 1 cm altura) embebida según diseño
(G03)	SIN GUARDAESCOBAS

ESPECIFICACIONES GENERALES	
(E01)	ALBARDILLAS PROTECCIÓN MUROS EN CONCRETO A = 0,25 m reforzado de 2500 PSI incluye refuerzo
(E02)	SUMINISTRO E INST. SISTEMA DE IMPERMEABILIZACIÓN POR IMPREG. DE PLACA Membrana elastomérica multicapa monolítica y fundida en sitio con refuerzo en malla estructurada o + poliest. de alto calibre impermeable+ recubrimiento en sílice de cuarz.
(E03)	CUBIERTA EN TEJA DE 505 MM CAL. 26 EN CALIDAD STANDING SEAM similar o de características técnicas superiores - Incluye instalación y suministro de todos los accesorios requeridos para el correcto montaje. Color verde RAL 6005
(E04)	FLANCHE EN LAMINA GALVANIZADA CAL. 20 d/0.70 M Suministro e instalación con wash primer + esmalte color verde RAL 6005 + anclaje a muro + sikaflex 1A)
(E05)	LAMINA GALVANIZADA CAL. 18 TIPO ACESCO O EQUIVALENTE Para caballete - desarrollo 100 m, incluye anclaje a viga + Sikaflex, incluye todos los elementos para su correcto montaje + pintura esmalte color verde RAL 6005
(E06)	CÁRCAMO PARA CABLEADO ELÉCTRICO EN PLACA DE CONTRAPISO Según diseño estructural
(E07)	MALLA ONDULADA CAL. 12 de 2 x 1 1/2" + ANGULO 1 1/2 x 1 1/2 x 1/4" + ANTICORROSIVO + PINTURA ELECTROESTATICA Suministro e instalación a todo costo. Incluye el suministro de todos los accesorios requeridos para el correcto montaje.
(E08)	ESCOTILLA PARA MANTENIMIENTO DE CUBIERTA EN LAMINA DE ALFAJOR Dimensiones: 1,00x1,00m efectivos con pendiente a 4 aguas. arra lisa 3/8".
(E09)	DESFOGUE DE PLANTA ELÉCTRICA SEGÚN DISEÑO ELÉCTRICO Murete de protección en bloque No 5, H= 0,80m, acabado en pintura acrílica ext. color marfil - RAL 1014; unión entre murete y desfogue en flanche en lámina galvanizada Cal. 20, acabado en wash primer + esmalte color gris RAL 9006 fijación con Sikaflex
(E10)	ALFAJÍA EN CONCRETO DE 2.500 PSI Ancho variable, según diseño (Incluye refuerzo). Acabado en pintura Koraza color gris RAL 9006
(E11)	MARCO DE VENTANA EN COLUMNETA DE CONCRETO DE 3.000 PSI Refuerzo según diseño estructural - acabado en pintura koraza color gris RAL 9006
(E12)	REJILLA EN LAMINA COLD ROLLED enmarcada en angulo de 1"x 1" cal. 18, persiana en lamina cold Rolled color negro mate
(E13)	SUNMISTRO E INSTALACION GARGOLA PREFABRICADA EN CONCRETO (Dimensiones 0,13x0,13x0,25m)