




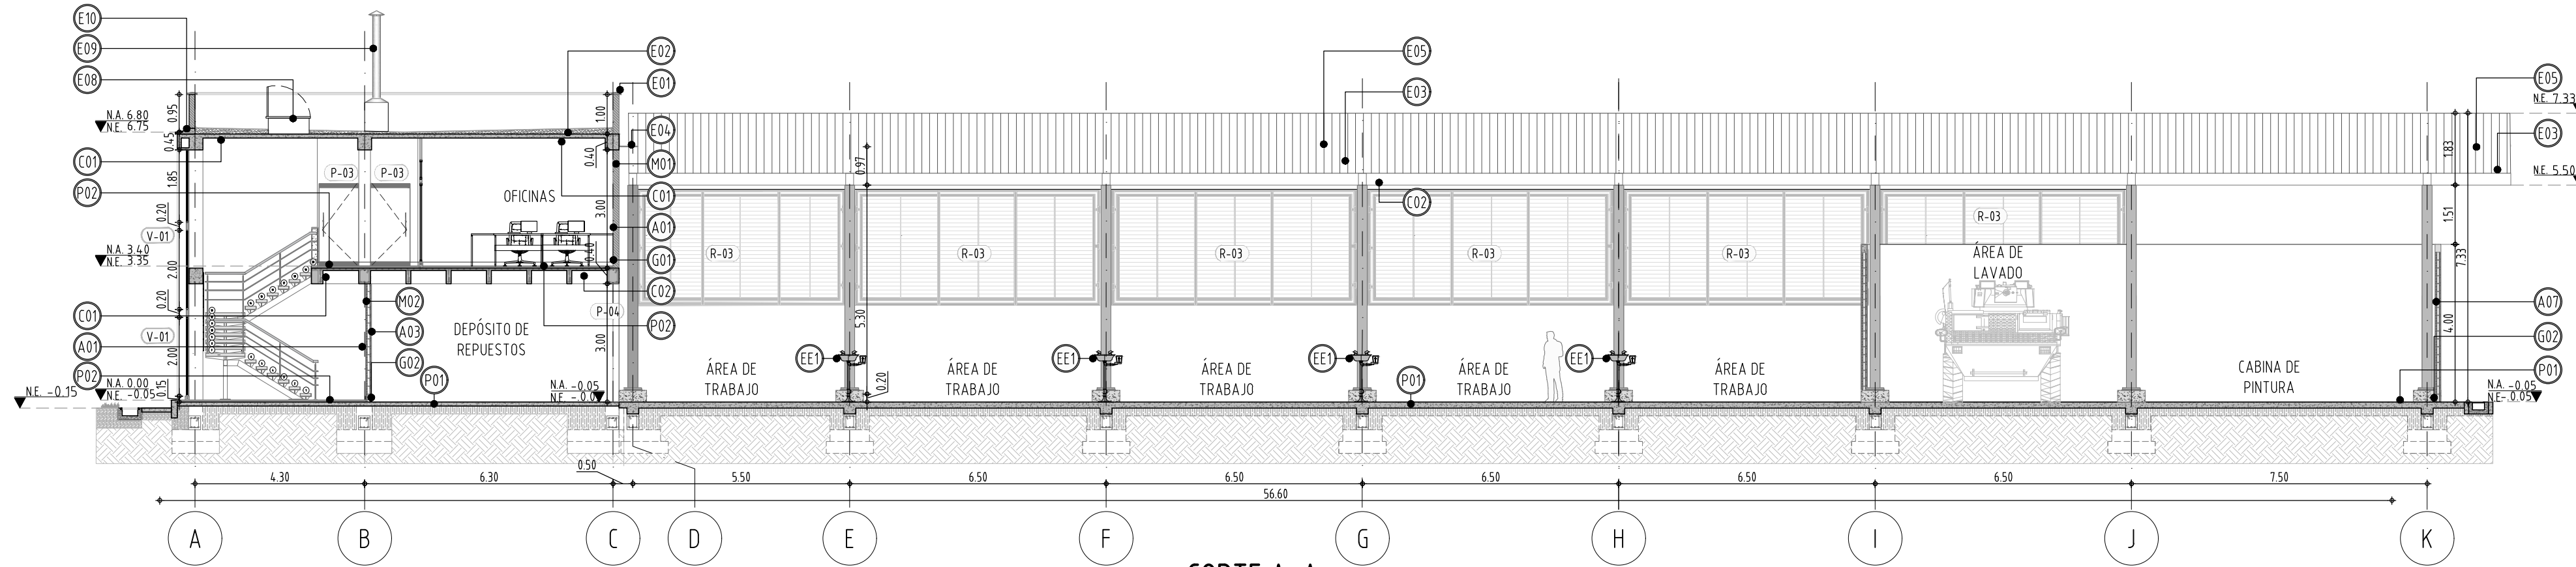

CORTE A-A
ESCALA 1:125

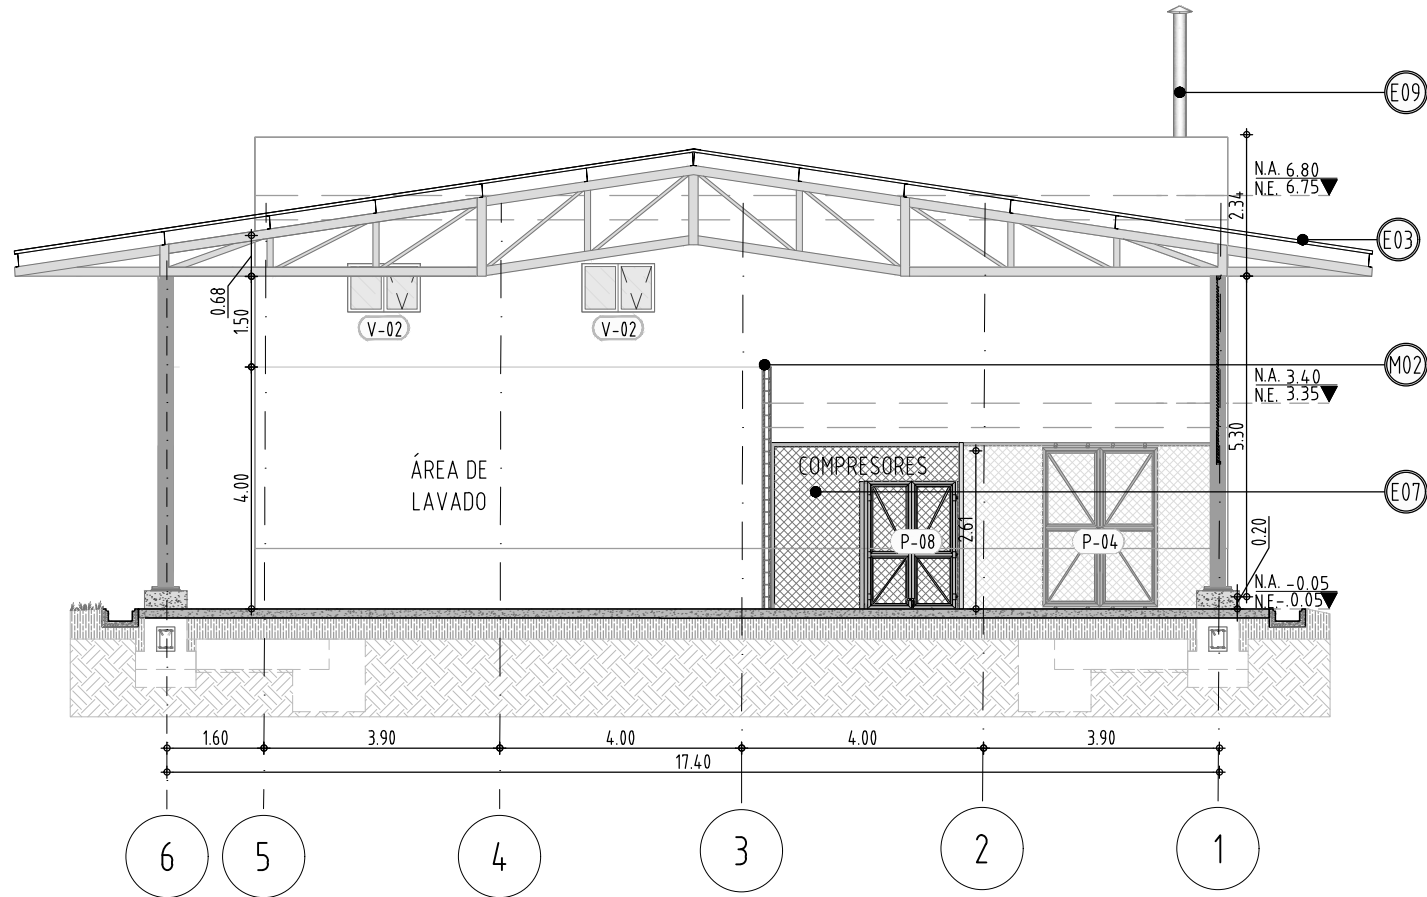

CORTE C-C
ESCALA 1:125

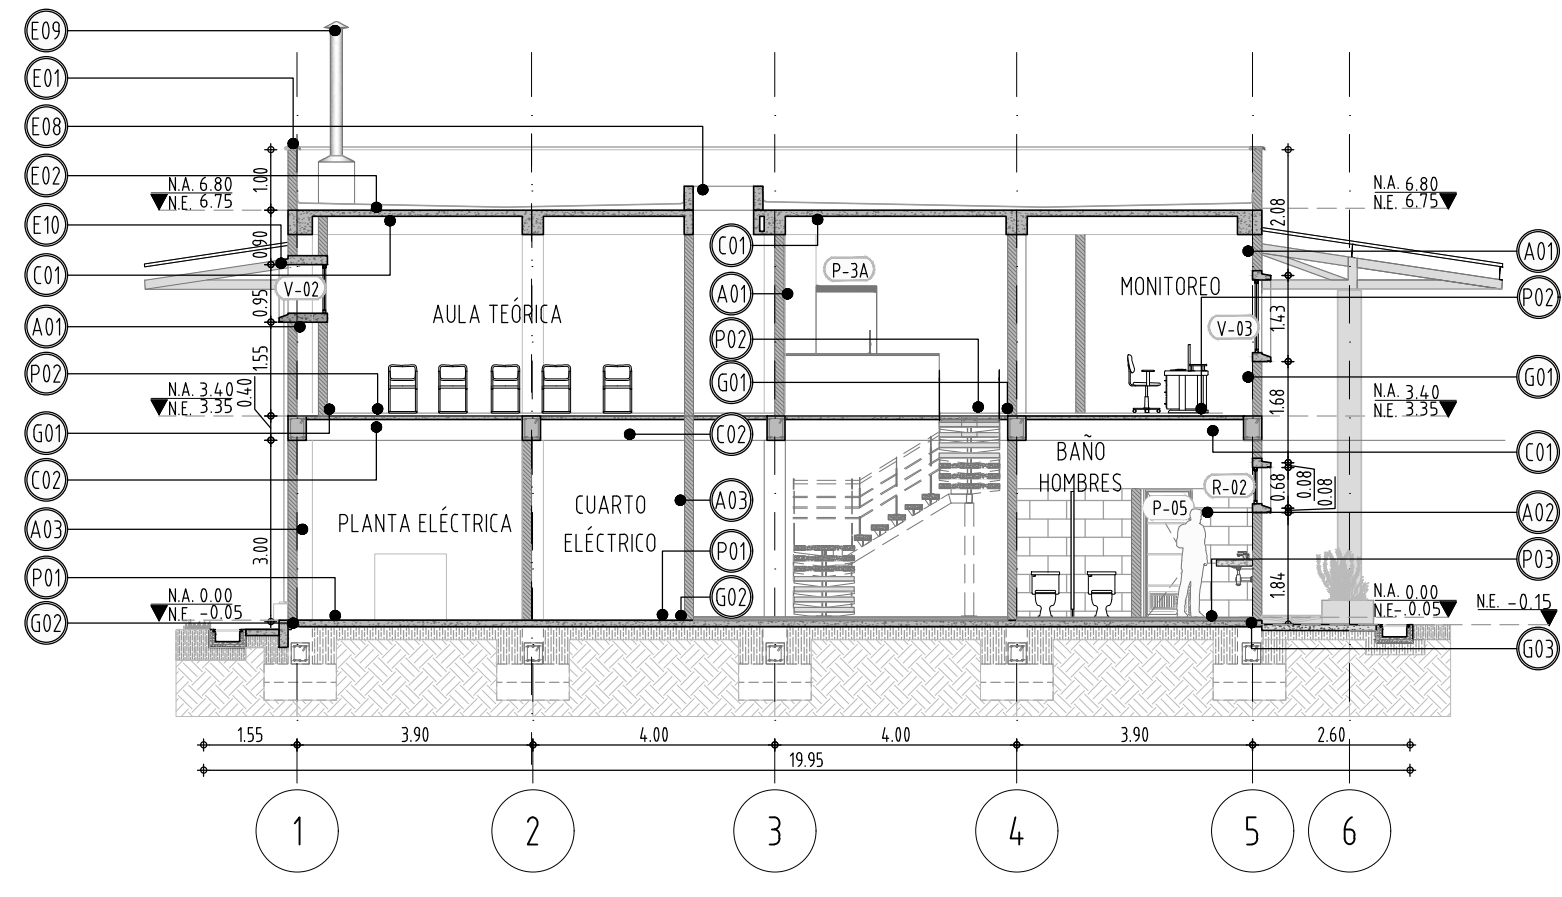

CORTE B-B
ESCALA 1:125

ACABADOS DE MUROS

(M01)	MURO EN BLOQUE No. 5 Arcilla 33x23x11.5 cm. Incluye mortero de pega y grafil 5 mm.
(M02)	MURO EN BLOQUE CONCRETO ESTRUCTURAL LISO 12x19x39 cm. Incluye mortero de pega y grafil
(A01)	PANETE LISO 1:3 INT. + ESTUCO Y VINILO 3 MANOS SOBRE MURO INT. (Incluye estuco, 1 mano en pintura tipo 2 y dos manos en pintura tipo 1, filos y dilataciones) - color blanco almendra.
(A02)	PANETE LISO 1:3 IMPERMEABILIZADO + CERÁMICA HD BLANCO SATINADO Incluye boquilla blanca y pegante - Altura de instal. hasta H= 2,10 m. según diseño. + estuco plástico y pintura epóxica a 3 manos sobre muro int. desde H=2,10 m. hasta nivel de borde inferior de vigas de placa superior - color blanco almendra.
(A03)	ESTUCO PLÁSTICO Y PINTURA EPÓXICA A 3 MANOS SOBRE MURO INT. Incluye estuco plástico, una mano en pintura tipo 2 y dos manos en pintura epoxi poliámda, base de agua, con catalizador, filos y dilataciones - color blanco almendra. sobre panete liso 1:3 impermeabilizado.
(A04)	PINTURA ACRILICA PARA EXTERIORES (5 años) 3 MANOS FACHADAS Incluye 1 mano en pintura tipo 2 y dos manos en pintura Acrilica para exteriores (5 años), filos y dilataciones. Color marfil - RAL 1014 sobre panete impermeabilizado.
(A05)	PINTURA ACRILICA PARA EXTERIORES (5 años) 3 MANOS FACHADAS Incluye 1 mano en pintura tipo 2 y dos manos en pintura Acrilica para exteriores (5 años), filos y dilataciones. Color verde ciprés, RAL 6011 sobre panete imperm.
(A06)	PINTURA ACRILICA PARA EXTERIORES (5 años) 3 MANOS FACHADAS Incluye 1 mano en pintura tipo 2 y dos manos en pintura Acrilica para exteriores (5 años), filos y dilataciones. Color gris oscuro RAL 7012 sobre panete imperm.
(A07)	PINTURA ACRILICA PARA EXTERIORES (5 años) 3 MANOS FACHADAS Incluye 1 mano en pintura tipo 2 y dos manos en pintura Acrilica para exteriores (5 años), filos y dilataciones. Color gris RAL 9006 sobre panete impermeabilizado.

ACABADOS DE CIELORASOS

(C01)	PINTURA EPOXICA ALTA RESISTENCIA CON CATALIZADOR 3 MANOS Bajo Placa Incluye 1 mano en pintura tipo 2 y dos manos en pintura epoxi poliámda con catalizador, filos y dilataciones, incluye resane y maquillaje de torta inferior
(C02)	SIN CIELORASO


ACABADOS DE PISOS Y GUARDAESCOBAS

(P01)	ENDURECEDOR COLOR (TONOS SEGÚN DISEÑO EN PLANO DE PISOS) Losas en concreto tipo Rocktop de Toxement o equivalente, acabado con allanadora metálica + pintura de señalización (según plano de pisos)
(P02)	PISO EN GRANO DE MÁRMOL GRAN TERRAZO GRIS CEARA color gris claro 40 x 60 cm. SKU 225026342 Ref. Alfa, equivalente o superior (incluye destroncada, pulida y brillada, mortero de nivelación y dilatación en bronce).
(P03)	CERÁMICA MYSTIC GRIS LISA 30,5 X 60 CM. Incluye boquilla gris claro y pegante + alisado de piso en mortero 1:4 impermeabilizado E= 0.04 m - disposición según diseño.
(G01)	GUARDAESCOBA RECTO EN BALDOSA GRANO DE MÁRMOL PCL 5 Color negro san gil 40 x 10 cm. (incluye boquilla y mortero de pega)
(G02)	GUARDAESCOBA EN PINTURA ESMALTE NEGRO MATE - H= 10 cm. Dilatación en panete 12cms prof x 1 cm atural embebida según diseño
(G03)	SIN GUARDAESCOBAS

ESPECIFICACIONES GENERALES

(E01)	ALBARDILLAS PROTECCIÓN MUROS EN CONCRETO A = 0,25 m reforzado de 2.500 PSI incluye refuerzo	(E09)	DESFOGUE DE PLANTA ELÉCTRICA SEGÚN DISEÑO ELÉCTRICO Murete de protección en bloque No.5, H= 0,80m, acabado en pintura acrílica ext. color marfil - RAL 1014, unión entre murete y desfogue en flanche en lámina galvanizada Cal. 20, acabado en wash primer + esmalte color gris RAL 9006 fijación con Sikaflex
(E02)	SUMINISTRO E INST. SISTEMA DE IMPERMEABILIZACIÓN POR IMPREG. DE PLACA Membra elastomérica multicapa monolítica y fundida en sitio con refuerzo en malla estructurada o + poliest. de alto calibre impermeable+ recubrimiento en sílice de cuarz.	(E10)	ALFAJÍA EN CONCRETO DE 2.500 PSI Ancho variable, según diseño (Incluye refuerzo). Acabado en pintura Koraza color gris RAL 9006
(E03)	CUBIERTA EN TEJA DE 505 MM CAL. 26 EN CALIDAD STANDING SEAM similar o de características técnicas superiores - Incluye instalación y suministro de todos los accesorios requeridos para el correcto montaje. Color verde RAL 6005	(E11)	MARCO DE VENTANA EN COLUMNETA DE CONCRETO DE 3.000 PSI Refuerzo según diseño estructural - acabado en pintura koraza color gris RAL 9006
(E04)	FLANCHE EN LAMINA GALVANIZADA CAL. 20 d/0.70 M Suministro e instalación con wash primer + esmalte color verde RAL 6005 + anclaje a muro + sikaflex 1A)	(E12)	REJILLA EN LAMINA COLD ROLLED enmarcada en angulo de 1"x 1" cal. 18, persiana en lamina cold Rolled color negro mate
(E05)	LAMINA GALVANIZADA CAL. 18 TIPO ASCESCO O EQUIVALENTE Para caballete - desarrollo 1,00 m, incluye anclaje a viga + Sikaflex, incluye todos los elementos para su correcto montaje + pintura esmalte color verde RAL 6005	(E13)	SUMINISTRO E INSTALACION GARGOLA PREFABRICADA EN CONCRETO (Dimensiones 0,13x0,13x0,25m)
(E06)	CÁRCAMO PARA CABLEADO ELÉCTRICO EN PLACA DE CONTRAPISO Según diseño estructural	(EE1)	SUMINISTRO E INSTALACIÓN DE LAVAJOS DE EMERGENCIA TIPO PEDESTAL en acero inoxidable y ABS de alta visibilidad, tipo industrial, con tapas protectoras de los aspersores evitan la acumulación de polvo o contaminantes.
(E07)	MALLA ONDULADA CAL. 12 de 2 x 1 1/2" + ANGULO 1 1/2 x 1 1/2 x 1/4" + ANTICORROSIVO + PINTURA ELECTROESTATICA Suministro e instalación a todo costo. Incluye el suministro de todos los accesorios requeridos para el correcto montaje.	CONVENCIÓN DE MUROS	
(E08)	ESCOTILLA PARA MANTENIMIENTO DE CUBIERTA EN LAMINA DE ALFAJOR Dimensiones: 1,00x1,00m efectivos con pendiente a 4 aguas. arra lisa 3/8".	(M01)	MURO EN BLOQUE No. 5 Arcilla 33x23x11.5 cm. Incluye mortero de pega y grafil 5 mm.
		(M02)	MURO EN BLOQUE CONCRETO ESTRUCTURAL LISO 12x19x39 cm. (Incluye mortero de pega y grafil)

EJÉRCITO NACIONAL DE COLOMBIA COMANDO DE INGENIEROS

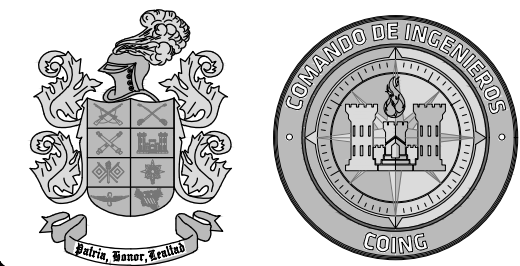

REVISIONES		
MODIFICACIONES	FECHA	
-	-	-
-	-	-
-	-	-
-	-	-

ARCHIVO DIGITAL:
SECCIÓN DE MMTO GMPHAZ.dwg

NOTA GENERAL DE PROYECTO:
- TODA MEDIDA DEBE SER VERIFICADA EN OBRA
- EN CASO DE ENCONTRARSE ALGUNA INCONSISTENCIA EN PLANOS, EL CONSTRUCTOR DEBE INFORMAR OPORTUNAMENTE AL COMANDO PARA SU REVISIÓN Y CORRESPONDIENTE AJUSTE, EN CASO DE SER NECESARIO.

DIBUJO:
NATALIA ANDREA RAMÍREZ DÍAZ
Mat. Prof. No. 439662024-101076892

REVISOR:
Arq. RAÚL RAMÍREZ RODRÍGUEZ
Mat. Prof. No. 425712009-10883913

DISEÑADOR:
ARQ. LINA PAOLA RODRÍGUEZ
Mat. Prof. No. 43462022-110525756

OFICIAL DE DISEÑO DE PROYECTOS DE INGENIEROS:
MY. Arq. CAMILO ANDRÉS CASTILLO GONZÁLEZ
Mat. Prof. No. 425712009-10728272

OFICIAL REVISOR DE ARQUITECTURA C-10:
Arq. MY. MARIO LASSO MORENO
Mat. Prof. No. 471722008-150108713

OFICIAL C-10:
CR. JOHN HENRNEY ESTEPA RÍOS
CC. No. 74162282

ESTE DOCUMENTO ES PROPIEDAD DEL EJÉRCITO NACIONAL DE COLOMBIA Y SU REPRODUCCIÓN O DISTRIBUCIÓN ESTÁ PROHIBIDA POR EL COMANDO DEL EJÉRCITO

EL CONTENIDO DE ESTE DOCUMENTO NO PUEDE SER MODIFICADO SIN AUTORIZACIÓN ESCRITA POR EL COMANDO DE INGENIEROS DEL EJÉRCITO

ESCALA GRÁFICA:
ESCALA
1/125

PROYECTO:
SECCIÓN DE MANTENIMIENTO DE VEHÍCULOS BLINDADOS DE SEGUNDO NIVEL

UNIDAD-GUARNICIÓN:
BATALLÓN DE INFANTERÍA MECANIZADA N°5
"GENERAL HERMÓGENES MAZA"
Cucutá, Norte de Santander

CONTIENE:
CORTES

CONSECUTIVO Nº:
0100-00-26

FECHA:
Abril 2026

PLANO Nº:
AR301
de 28