


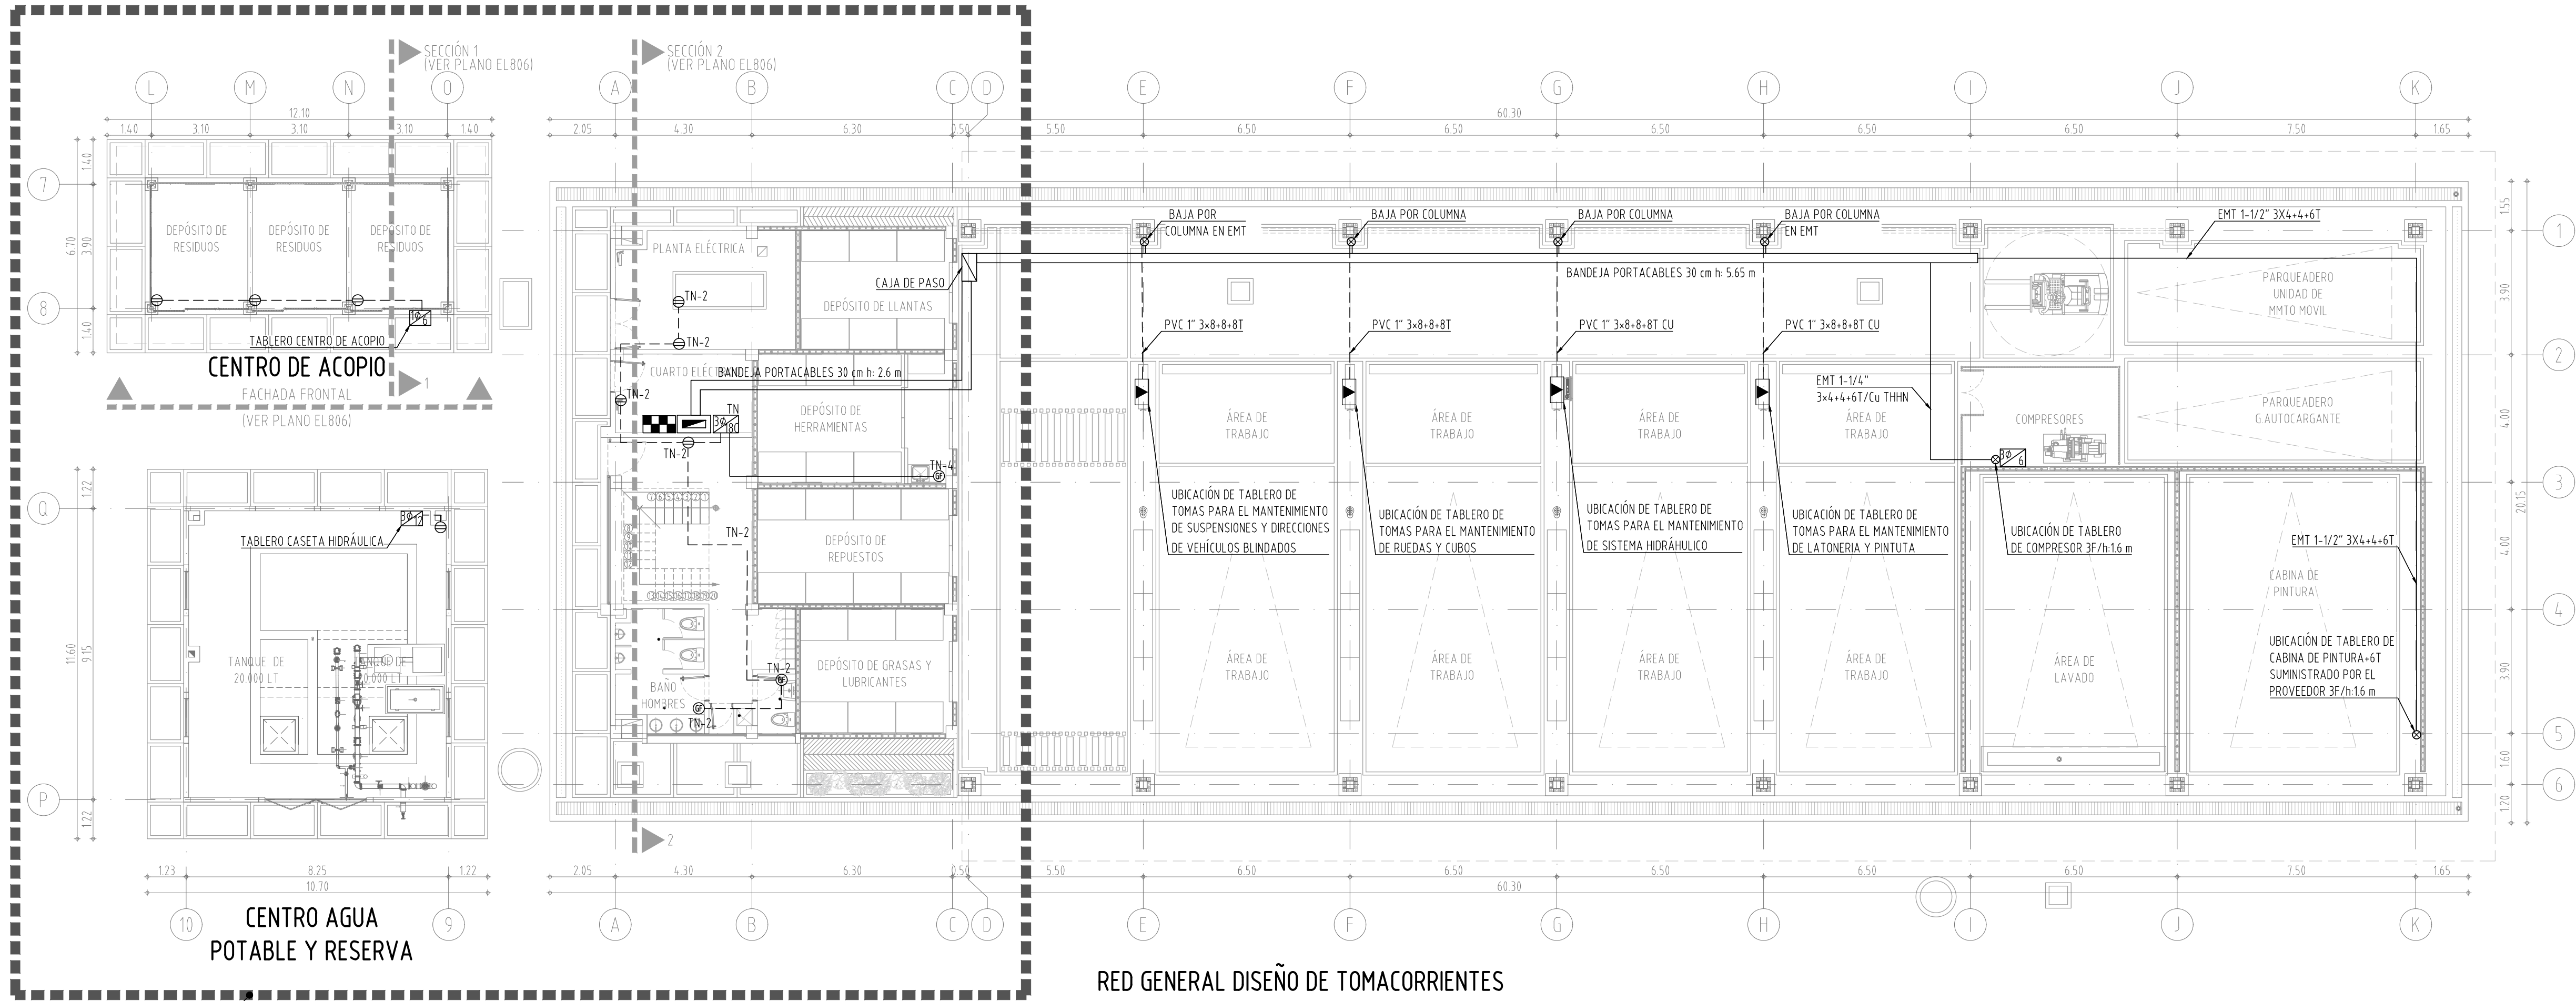

RED GENERAL DISEÑO DE TOMACORRIENTES
PLANTA PRIMER PISO
ESCALA.....1:125

VER "DISEÑO DE TOMACORRIENTES"
PLANTA PRIMER PISO"
PLANO EL805

NOTAS

- La empresa contratista en coordinación con el Ingeniero Interventor serán los responsables por el cumplimiento en general de la Norma NTC 2050, del Reglamento técnico de Instalaciones eléctricas "RETIE" y el Reglamento Técnico de Iluminación y Alumbrado Público "RETILAP".
- En este plano de tomacorrientes se ha indicado para las 4 áreas de trabajo de los hangares un "tablero instalado en muro" que aloja tres tipos de tomas diferentes, una bifásica, una trifásica y una monofásica, las cuales van dentro del tablero. (Ver detalle).
- Todos los tomacorrientes se instalarán a 30 cm a menos que se indique otra altura.
- Los tomacorrientes GFCI para baño se deben instalar a una altura de 1.2 metros.

CONVENCIONES

	Tablero eléctrico para interruptores automáticos tipo enchufables
	Tablero eléctrico tipo industrial
	Caja de paso de 20x20 cm
	Tablero instalado en muro, aloja toma 3F/2F/1F (Ver detalle)
	Tomacorriente doble monofásica 120 V, color blanca en muro
	Tomacorriente bifásica de pata trabada 30 amperios
	Tomacorriente trifásica 50 amperios
	Tomacorriente con protección de falla tierra 120V color blanca
	Toma de red regulada 120 voltios color naranja polo a tierra aislado
	Tubo que baja
	Tubo que sube
	Bandeja portacable descolgada de estructura metálica
	Canaleta metálica perimetral con división interna
	Tubo por piso
	Tubo por techo o muro