
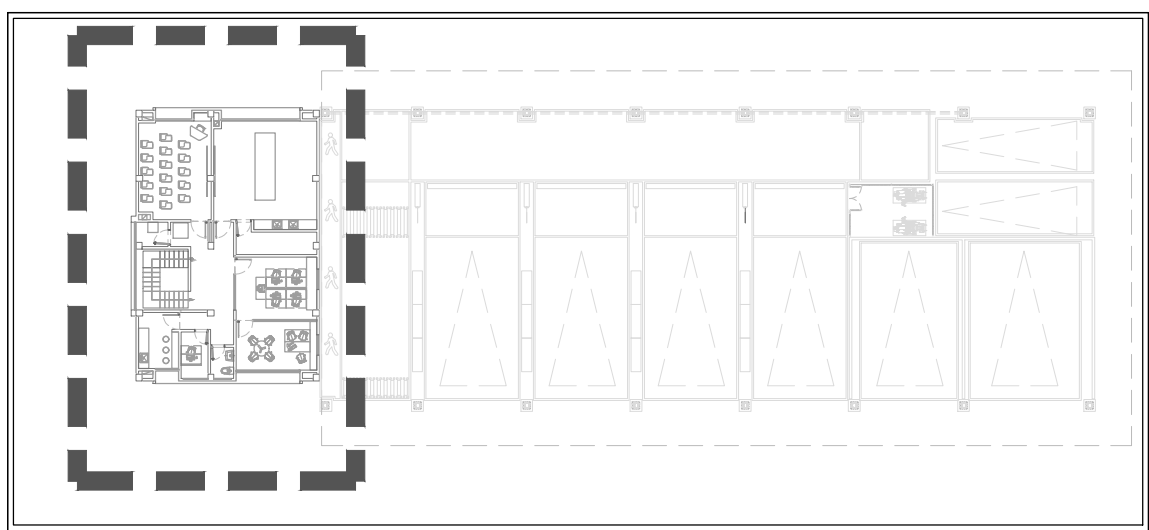


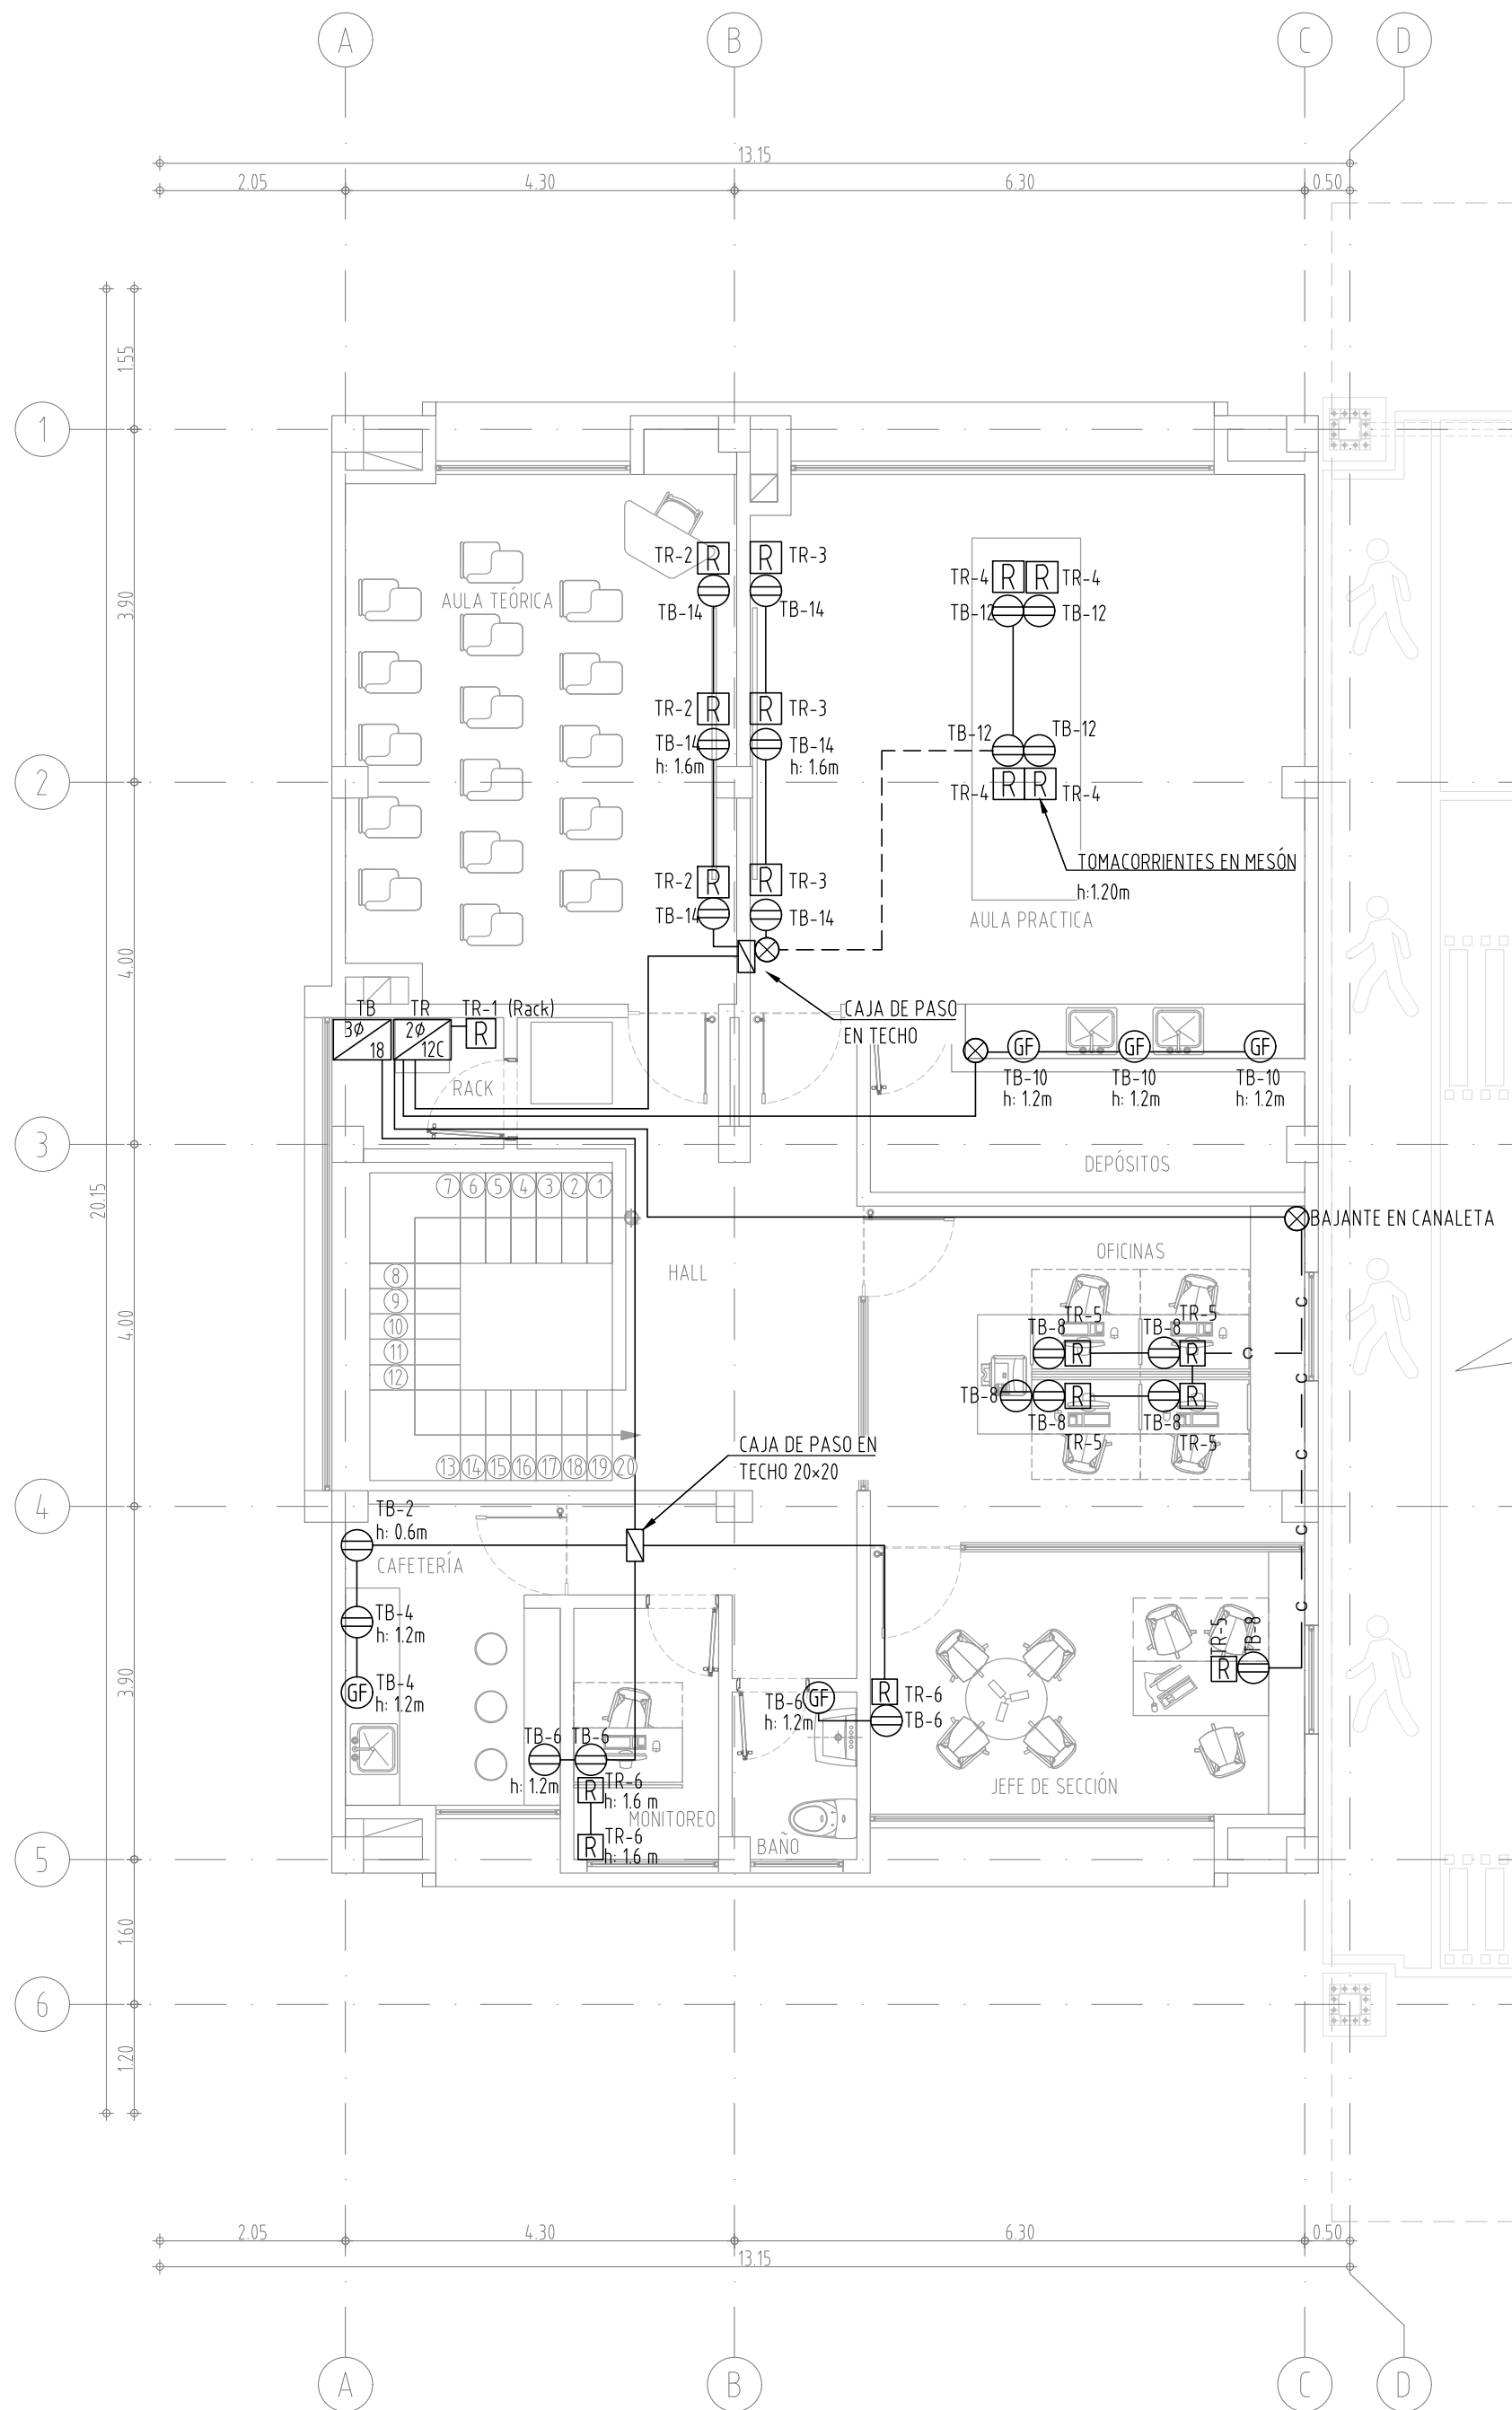

ESQUEMA PLANTA GENERAL  
SEGUNDO PISO


NOTAS

- La empresa contratista en coordinación con el Ingeniero Interventor serán los responsables por el cumplimiento en general de la Norma NTC 2050, del Reglamento técnico de Instalaciones eléctricas "RETE" y el Reglamento Técnico de Iluminación y Alumbrado Público "RETILAP".
- En este plano de tomacorrientes se ha indicado para las 4 áreas de trabajo de los hangares un "Tablero instalado en muro" que aloja tres tipos de tomas diferentes, una bifásica, una trifásica y una monofásica, las cuales van dentro del tablero. (Ver detalle).
- Todos los tomacorrientes se instalarán a 30 cm a menos que se indique otra altura.
- Los tomacorrientes GFCI para baño se deben instalar a una altura de 1.2 metros.

CONVENCIONES


|  |                                                                      |
|--|----------------------------------------------------------------------|
|  | Tablero eléctrico para interruptores automáticos tipo enchufables    |
|  | Tablero eléctrico tipo industrial                                    |
|  | Caja de paso de 20x20 cm                                             |
|  | Tablero instalado en muro, aloja toma 3F/2F/1F (Ver detalle)         |
|  | Tomacorriente doble monofásica 120 V, color blanca en muro           |
|  | Tomacorriente bifásica de pata trabada 30 amperios                   |
|  | Tomacorriente trifásica 50 amperios                                  |
|  | Tomacorriente con protección de falla tierra 120V color blanca       |
|  | Toma de red regulada 120 voltios color naranja polo a tierra aislado |
|  | Tubo que baja                                                        |
|  | Tubo que sube                                                        |
|  | Bandeja portable descolgada de estructura metálica                   |
|  | Canaleta metálica perimetral con división interna                    |
|  | Tubo por piso                                                        |
|  | Tubo por techo o muro                                                |

DISEÑO DE TOMACORRIENTES  
PLANTA SEGUNDO PISO  
ESCALA: 1:75

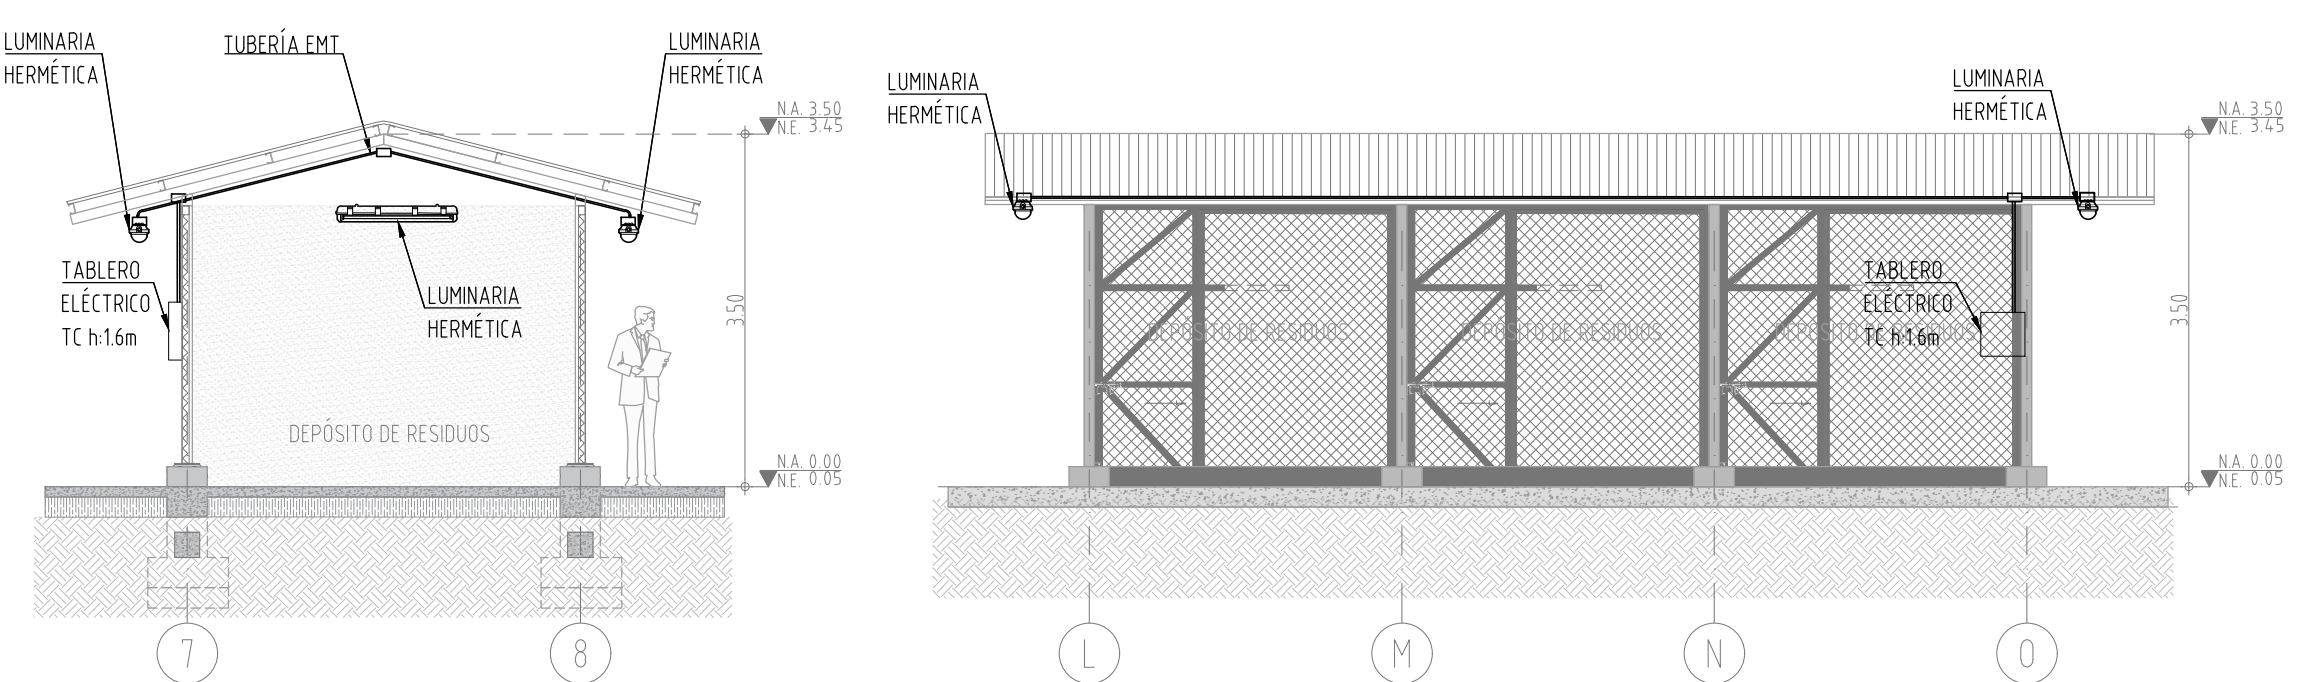

CENTRO DE ACOPIO  
SECCIÓN 1-1  
ESCALA 1:75

CENTRO DE ACOPIO  
FACHADA FRONTAL  
ESCALA 1:75

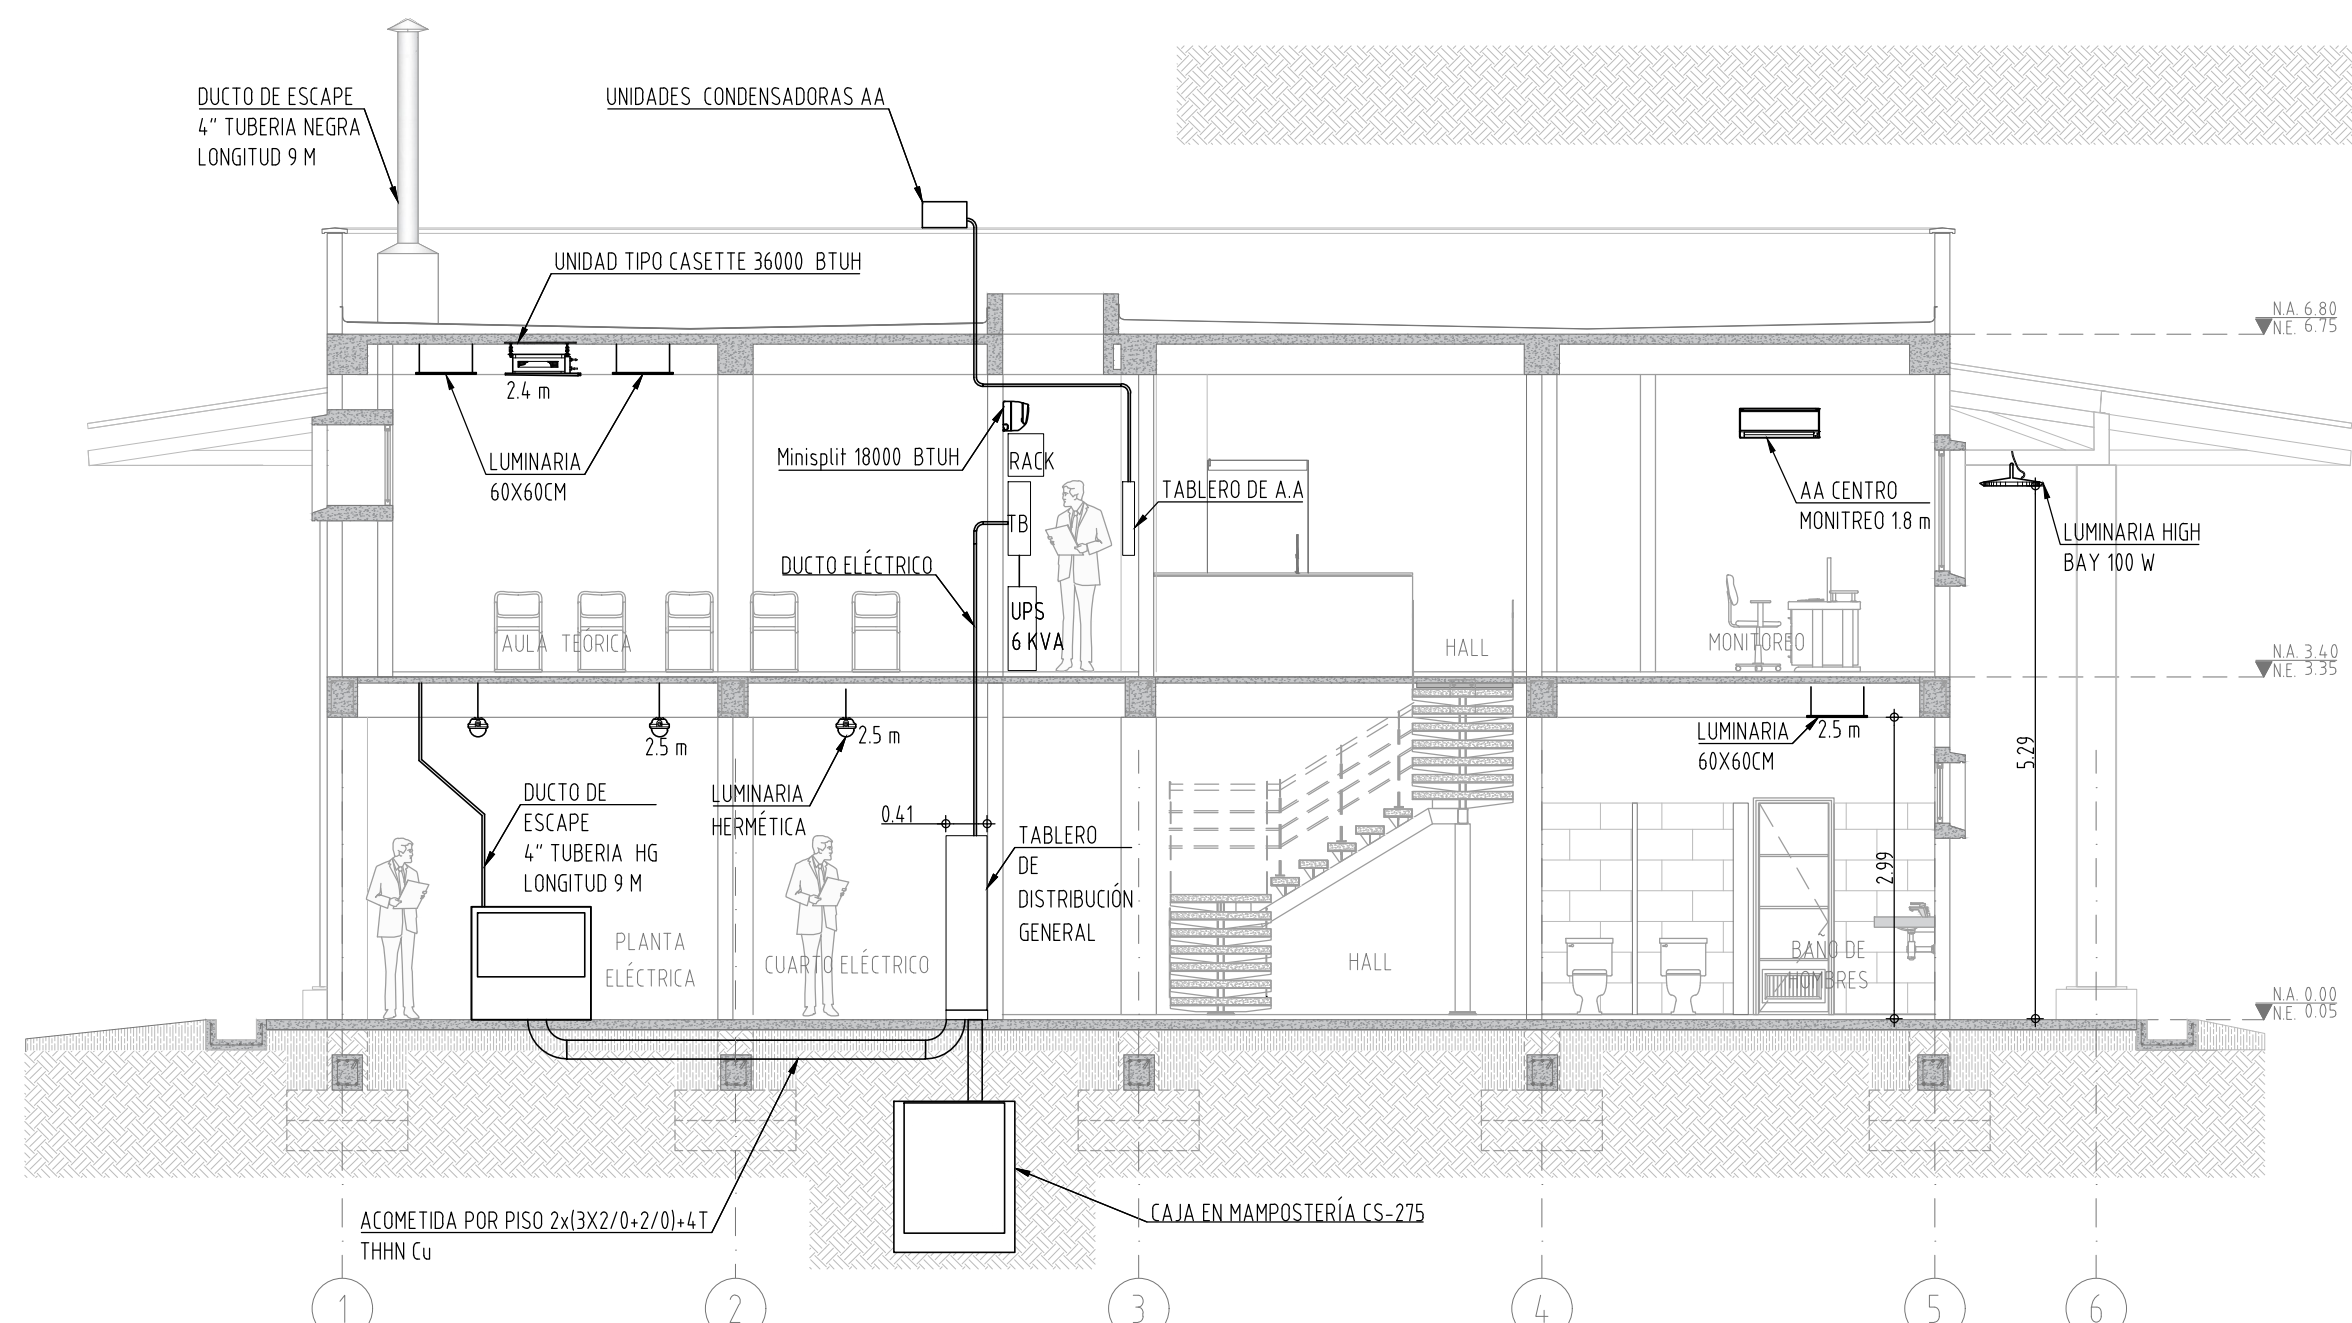

SECCIÓN 2-2  
ALTURA DE INSTALACIÓN DE EQUIPOS  
ESCALA 1:75