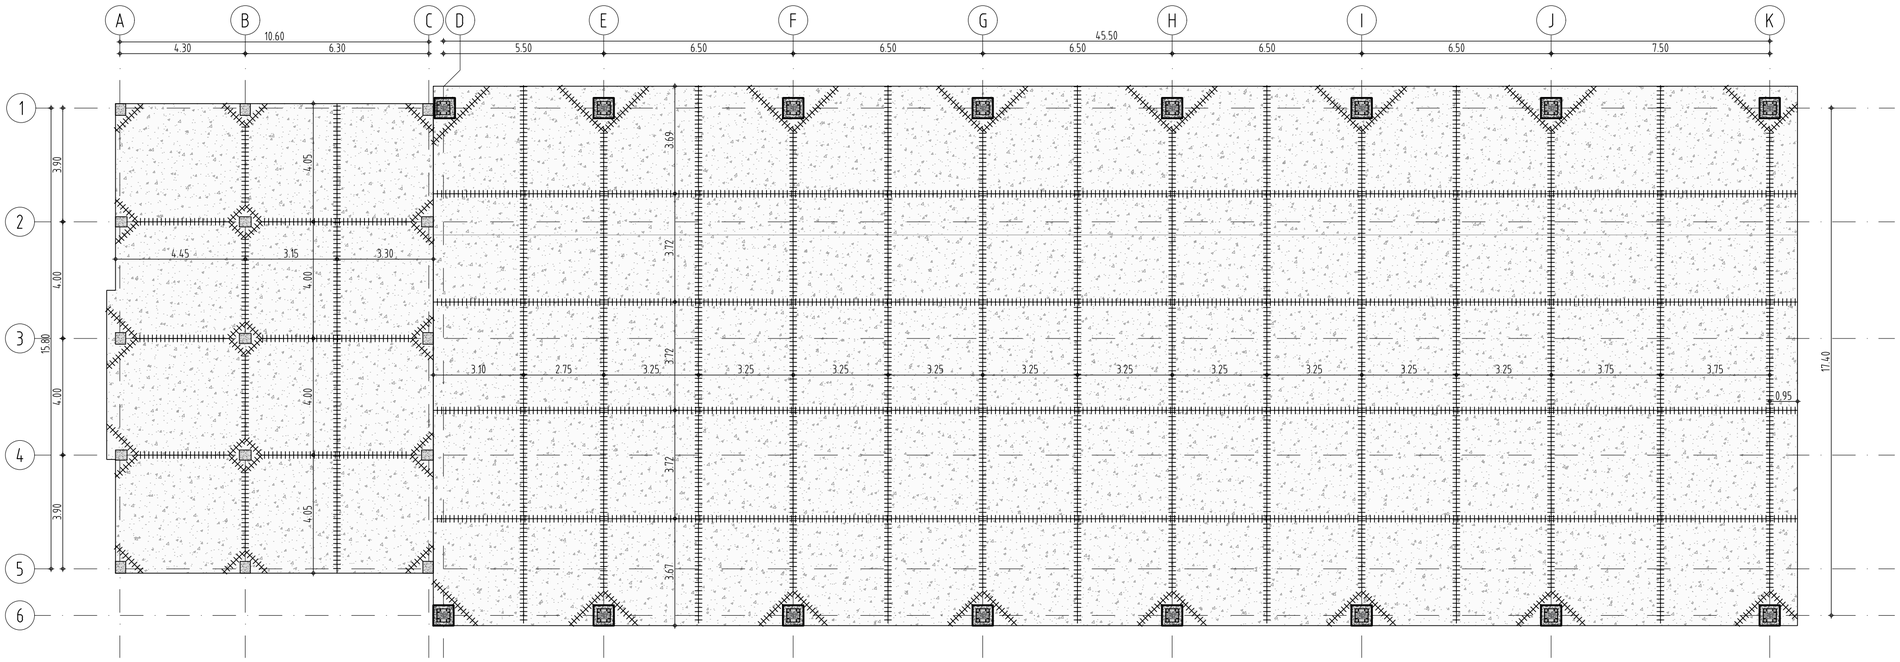

PLANTA DE JUNTAS DE CONSTRUCCIÓN BLOQUE DE SERVICIO Y HANGAR

ESC:1/125

NOTAS DE DISEÑO

1. Aa=0.35 Av=0.30 Fa= 1.05 Fv=1.50
2. Zona de amenaza sísmica: Alta
3. Grupo de uso: III
4. Coeficiente de importancia: I=1.25
5. Coeficiente de discipación de energia:
   Bloque de servisio R = 7
   Hangar R = 2.5
6. Capacidad portante del suelo:
   30.30 - 35.70 kN/m2 (zapatas aisladas.)
7. istema estructura:
   Guardia: Pórticos resistente a momento y péndulo invertido con capacidad de disipación de energia- (DES)

ESPECIFICACIONES :

Concreto cimentación : f'c=21.0 Mpa (Impermeabilizado)
Concreto losa contapiso.: f'c=21.1 Mpa (Impermeabilizado)
Concreto placa aérea: f'c=21.1 Mpa
Concreto de limpieza: f'c=17 Mpa
Concreto Columnas y vigas aéreas: f'c=21.1 Mpa
Concreto Columnetas y vigas de confinamiento: f'c=21.1 Mpa
Concreto columnas metalicas seccion compuestas: f'c=17.5 Mpa
RECUBRIMIENTOS
Vigas de cimentación: 5 cm
Vigas aéreas: 4 cm
Losas aéreas: 2.5 cm
Columnas: 4 cm
Zapatas: 7.5 cm
El cemento debe cumplir NTC 121 Y 321
Agregados según NTC 174
Acero de refuerzo: NTC 2289/ASTM A706 - fy=420 Mpa
Acero malla electrosoldada: NTC 5806 - fy=485 Mpa

NOTAS :

1. El presente diseño no es apto para suelos de arcillas expansivas, suelos erodables o licuables por lo tanto debe ser adaptado bajo las condiciones encontradas en sitio y dadas por el estudio de suelos para el proyecto. El estudio de suelos debe ser aprobado por el ingeniero calculista.
2. Cualquier modificación o equivalencia se debe consultar al calculista .
3. El diseño de la estructura se ha efectuado con base en el diseño arquitectónico, el constructor no podrá variar los espesores ni las dimensiones de los elementos, ni sobrecargar la estructura con cargas no previstas en el diseño.
4. El contratista deberá verificar previamente los planos arquitectónicos, hidraúlicos y eléctricos.
5. Todas las dimensiones y niveles deberán verificarse con los planos arquitectónicos y serán verficadas en obra por el constructor.
6. El acero de refuerzo debe verificarse en el sitio de emplazamiento antes de efectuar su corte.
7. Se deberán colocar los estribos rotando la ubicación de los ganchos a lo largo de los elementos.
8. La estabilidad de la obra durante el proceso de construcción serán propuestos por el contratista y aprobados por la interventoría.
9. El contratista deberá realizar los planos record de toda la estructura con base en los cambios de obra.
10. En caso de encontrar condiciones de cimentación diferentes a las descritas en el estudio de suelos deben ser reportadas para realizar los ajustes necesarios.
11. Antes de fundir los cimientos el constructor deberá verificar , con aprobación del supervisor, que el nivel portante corresponde al descrito en el estudio de suelos; en caso de diferir es necesario que sea reportado para realizar los ajustes correspondientes.
12. Se debe garantizar el recubrimiento de todos los elementos estructurales con el uso de distanciadores.

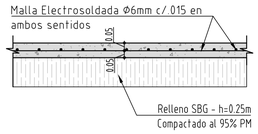

PLACA DE CONTRAPISO BLOQUE DE SERVICIOS

ESC:1/25

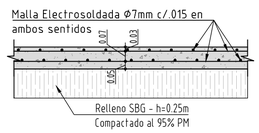

PLACA DE CONTRAPISO HANGAR

ESC:1/25

NOTAS :

1. El presente diseño no es apto para suelos de arcillas expansivas, suelos erodables o licuables por lo tanto debe ser adaptado bajo las condiciones encontradas en sitio y dadas por el estudio de suelos para el proyecto. El estudio de suelos debe ser aprobado por el ingeniero calculista.
2. Cualquier modificación o equivalencia se debe consultar al calculista .
3. El diseño de la estructura se ha efectuado con base en el diseño arquitectónico, el constructor no podrá variar los espesores ni las dimensiones de los elementos, ni sobrecargar la estructura con cargas no previstas en el diseño.
4. El contratista deberá verificar previamente los planos arquitectónicos, hidraúlicos y eléctricos.
5. Todas las dimensiones y niveles deberán verificarse con los planos arquitectónicos y serán verficadas en obra por el constructor.
6. El acero de refuerzo debe verificarse en el sitio de emplazamiento antes de efectuar su corte.
7. Se deberán colocar los estribos rotando la ubicación de los ganchos a lo largo de los elementos.
8. La estabilidad de la obra durante el proceso de construcción serán propuestos por el contratista y aprobados por la interventoría.
9. El contratista deberá realizar los planos record de toda la estructura con base en los cambios de obra.
10. En caso de encontrar condiciones de cimentación diferentes a las descritas en el estudio de suelos deben ser reportadas para realizar los ajustes necesarios.
11. Antes de fundir los cimientos el constructor deberá verificar , con aprobación del supervisor, que el nivel portante corresponde al descrito en el estudio de suelos; en caso de diferir es necesario que sea reportado para realizar los ajustes correspondientes.
12. Se debe garantizar el recubrimiento de todos los elementos estructurales con el uso de distanciadores.

EJÉRCITO NACIONAL DE COLOMBIA

COMANDO DE INGENIEROS

ISO 9001 SC6310-1

IQNET CERTIFIED MANAGEMENT SYSTEM

REVISIONES

	MODIFICACIONES	FECHA	
	-	-	
	-	-	
	-	-	

ARCHIVO DIGITAL:
ESTRUCTURA SERVICIOS Y HANGAR 2002N.dwg

NOTA GENERAL DE PROYECTO :
TODA MEDIDA DEBE SER VERIFICADA EN OBRA.
EN CASO DE ENCONTRARSE ALGUNA INCONSISTENCIA EN PLANOS, EL CONSTRUCTOR DEBE INFORMAR OPORTUNAMENTE A EL CONG PARA SU REVISIÓN Y CORRESPONDIENTE AJUSTE, EN CASO DE SER NECESARIO.

DIBUJO :
LINETH ALEXANDRA POLANCO F.
Tarjeta Prof. No. 126222019-101089558

REVISOR:
Arq. RAÚL RAMIREZ RODRIGUEZ.
Mat. Prof. No. A2571209-79885913

DISEÑADOR:
Arq. LINA PAOLA RODRIGUEZ MORENO
Mat. Prof. No. 2502-244528 CND

REVISOR:
Ing. Civil. IRWIN CAMILO CUBILLOS
Mat. Prof. No.25202-153086CND

DISEÑADOR:
Ing. Civil. JUAN CARLOS HERRERA
Mat. Prof. No. 132021-155411 BLV

OFICIAL DE DISEÑO DE PROYECTOS DE INGENIEROS:
MY. Arq. CAMILO ANDRES CASTILLO GONZALEZ
Mat. Prof. No.A2552004-80726272

OFICIAL REVISOR DE ARQUITECTURA C-10
MY.Arq. MARIO LASSO MORENO
Mat. Prof. No.A11712008-13010873

OFICIAL C-10 CONG
CR. JOHN HENRNEY ESTEPA RIOS
C.C. 4.182282

ESTE DOCUMENTO ES PROPIEDAD DEL EJÉRCITO NACIONAL DE COLOMBIA Y SU REPRODUCCIÓN O DISTRIBUCIÓN ESTA PROHIBIDA POR EL COMANDO DEL EJÉRCITO
EL CONTENIDO DE ESTE DOCUMENTO NO PUEDE SER MODIFICADO SIN AUTORIZACIÓN ESCRITA POR EL COMANDO DE INGENIEROS DEL EJÉRCITO

ESCALA GRÁFICA:
ESCALA:
Indicadas

PROYECTO :
SECCIÓN DE MANTENIMIENTO DE SEGUNDO NIVEL PARA VEHÍCULOS BLINDADOS

UNIDAD-GUARNICION :
GRUPO DE CABALLERÍA MECANIZADO No. 5 "GENERAL HERMÓGENES MAZA" GMMAZ
CUCUTÁ-NORTE DE SANTANDER

CONTIENE:
PLACA DE CONTRA PISO Y JUNTA DE CONSTRUCCÓN BLOQUE DE SERVICIOS Y HANGAR

CONSECUTIVO Nº
0120-00-26

FECHA:
ABRIL 2026

PLANO No.
ES604 DE 19