




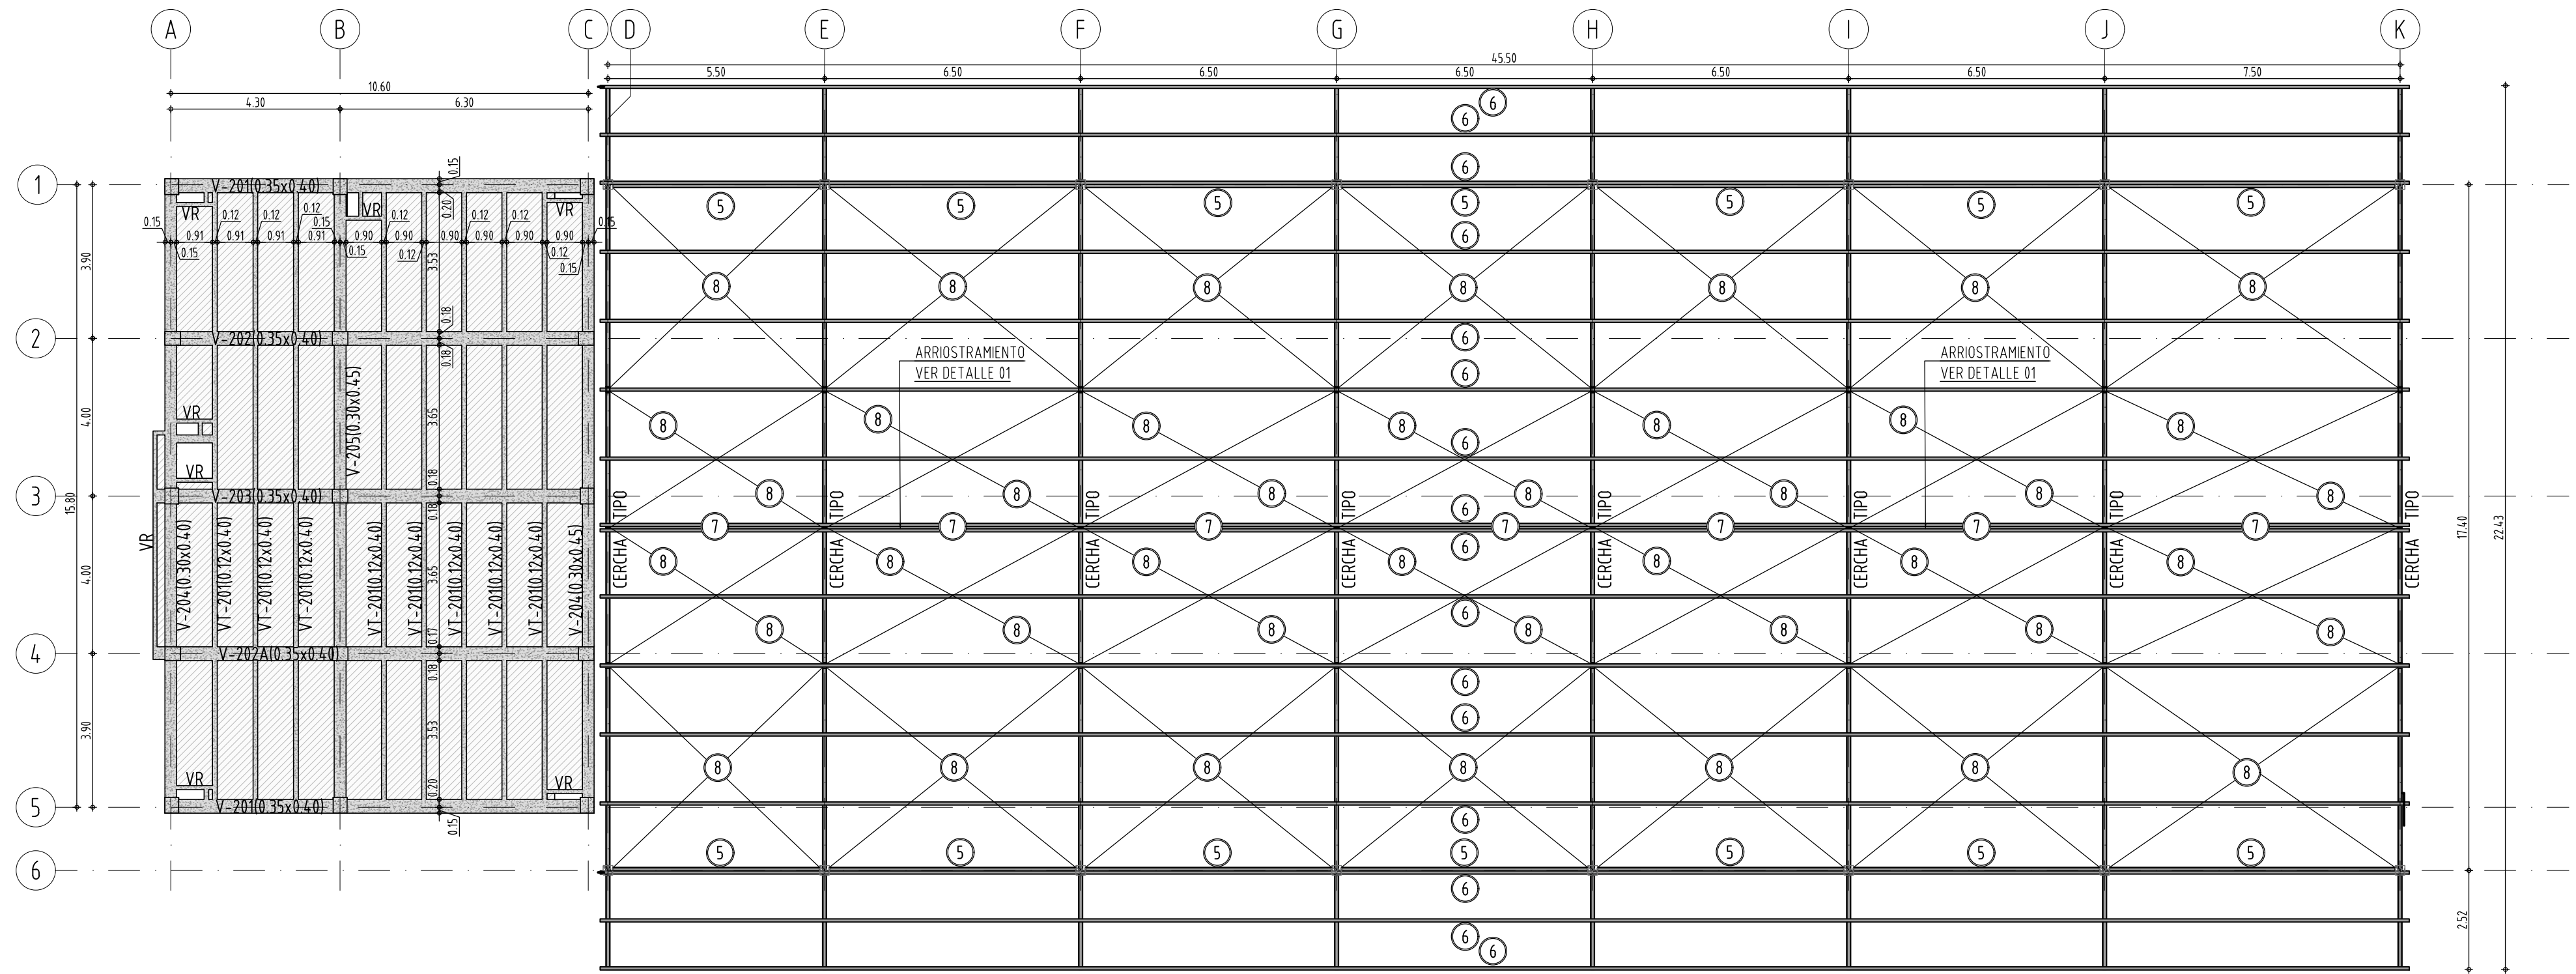

PLANTA DE CUBIERTA BLOQUE DE SERVICIO Y HANGAR
ESC:1/125

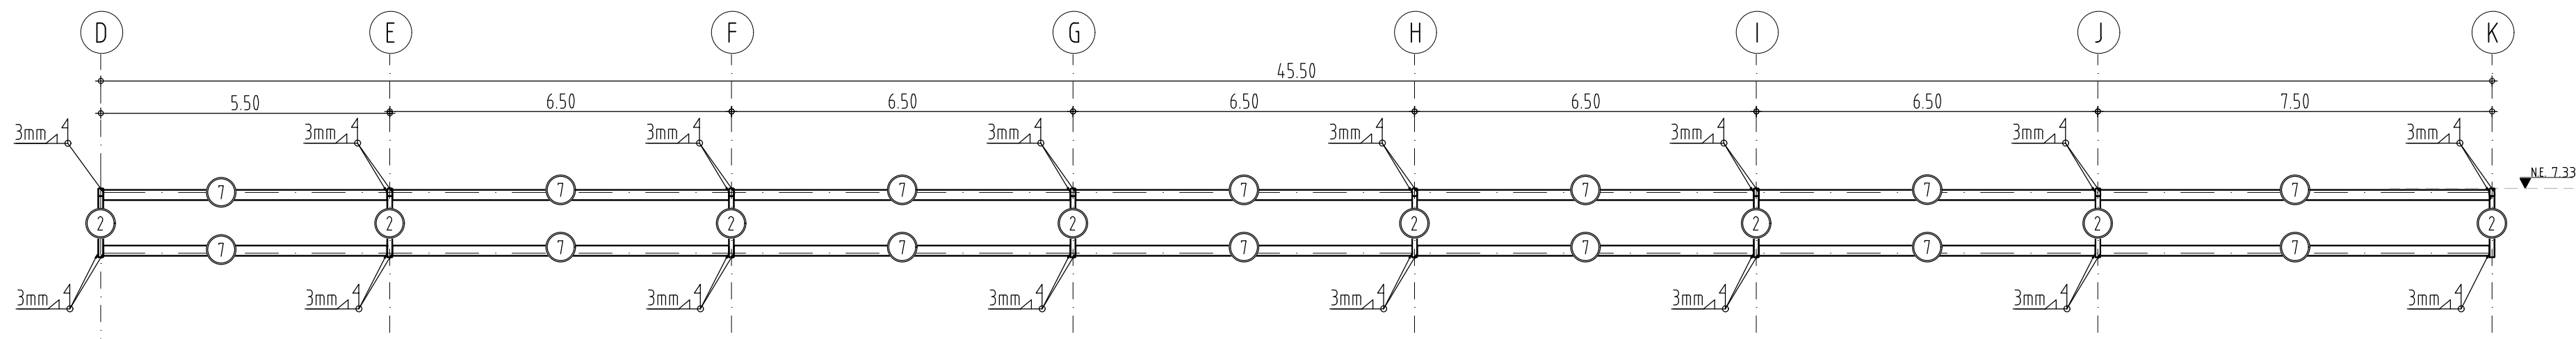

DETALLE 1 CORTE ARRIOSTRAMIENTO CERCHA (CENTRO)
ESC:1/100

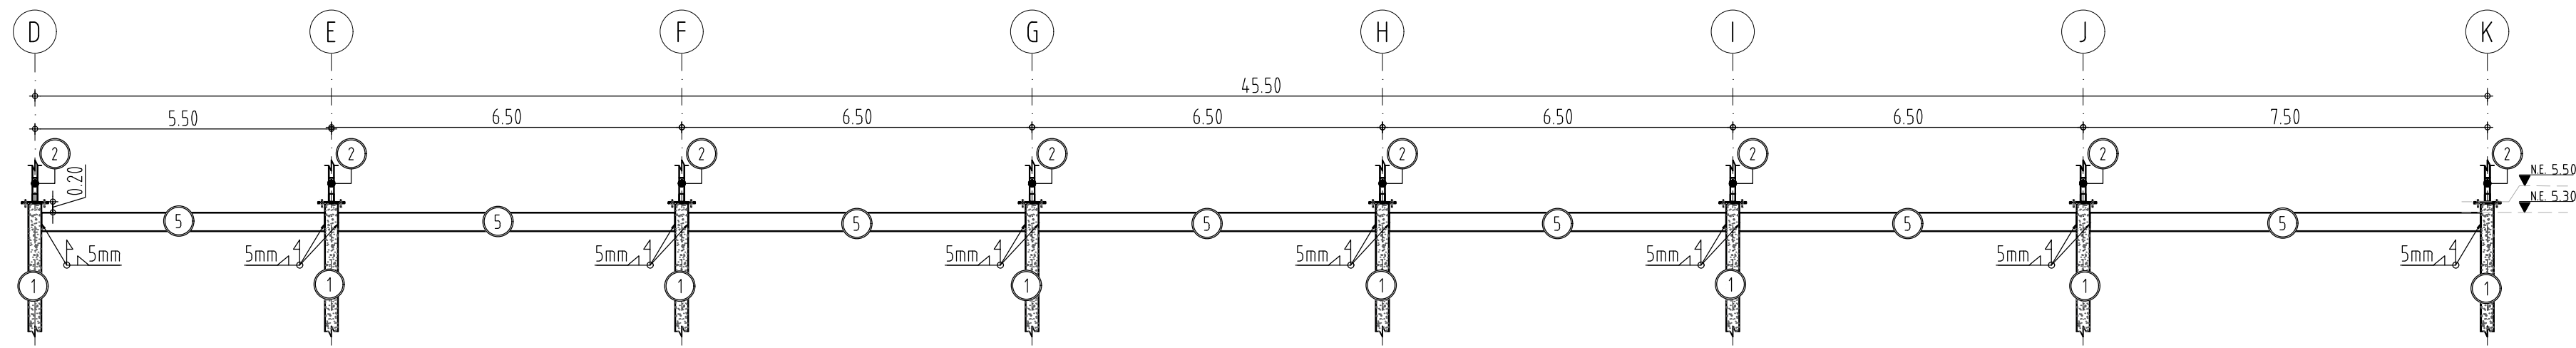

DETALLE 2 CORTE ARRIOSTRAMIENTO CERCHA EJE 1 Y 6
ESC:1/100